




PLANO DE INDEPENDIZACION

ESCALA : 1/750

301800


302000

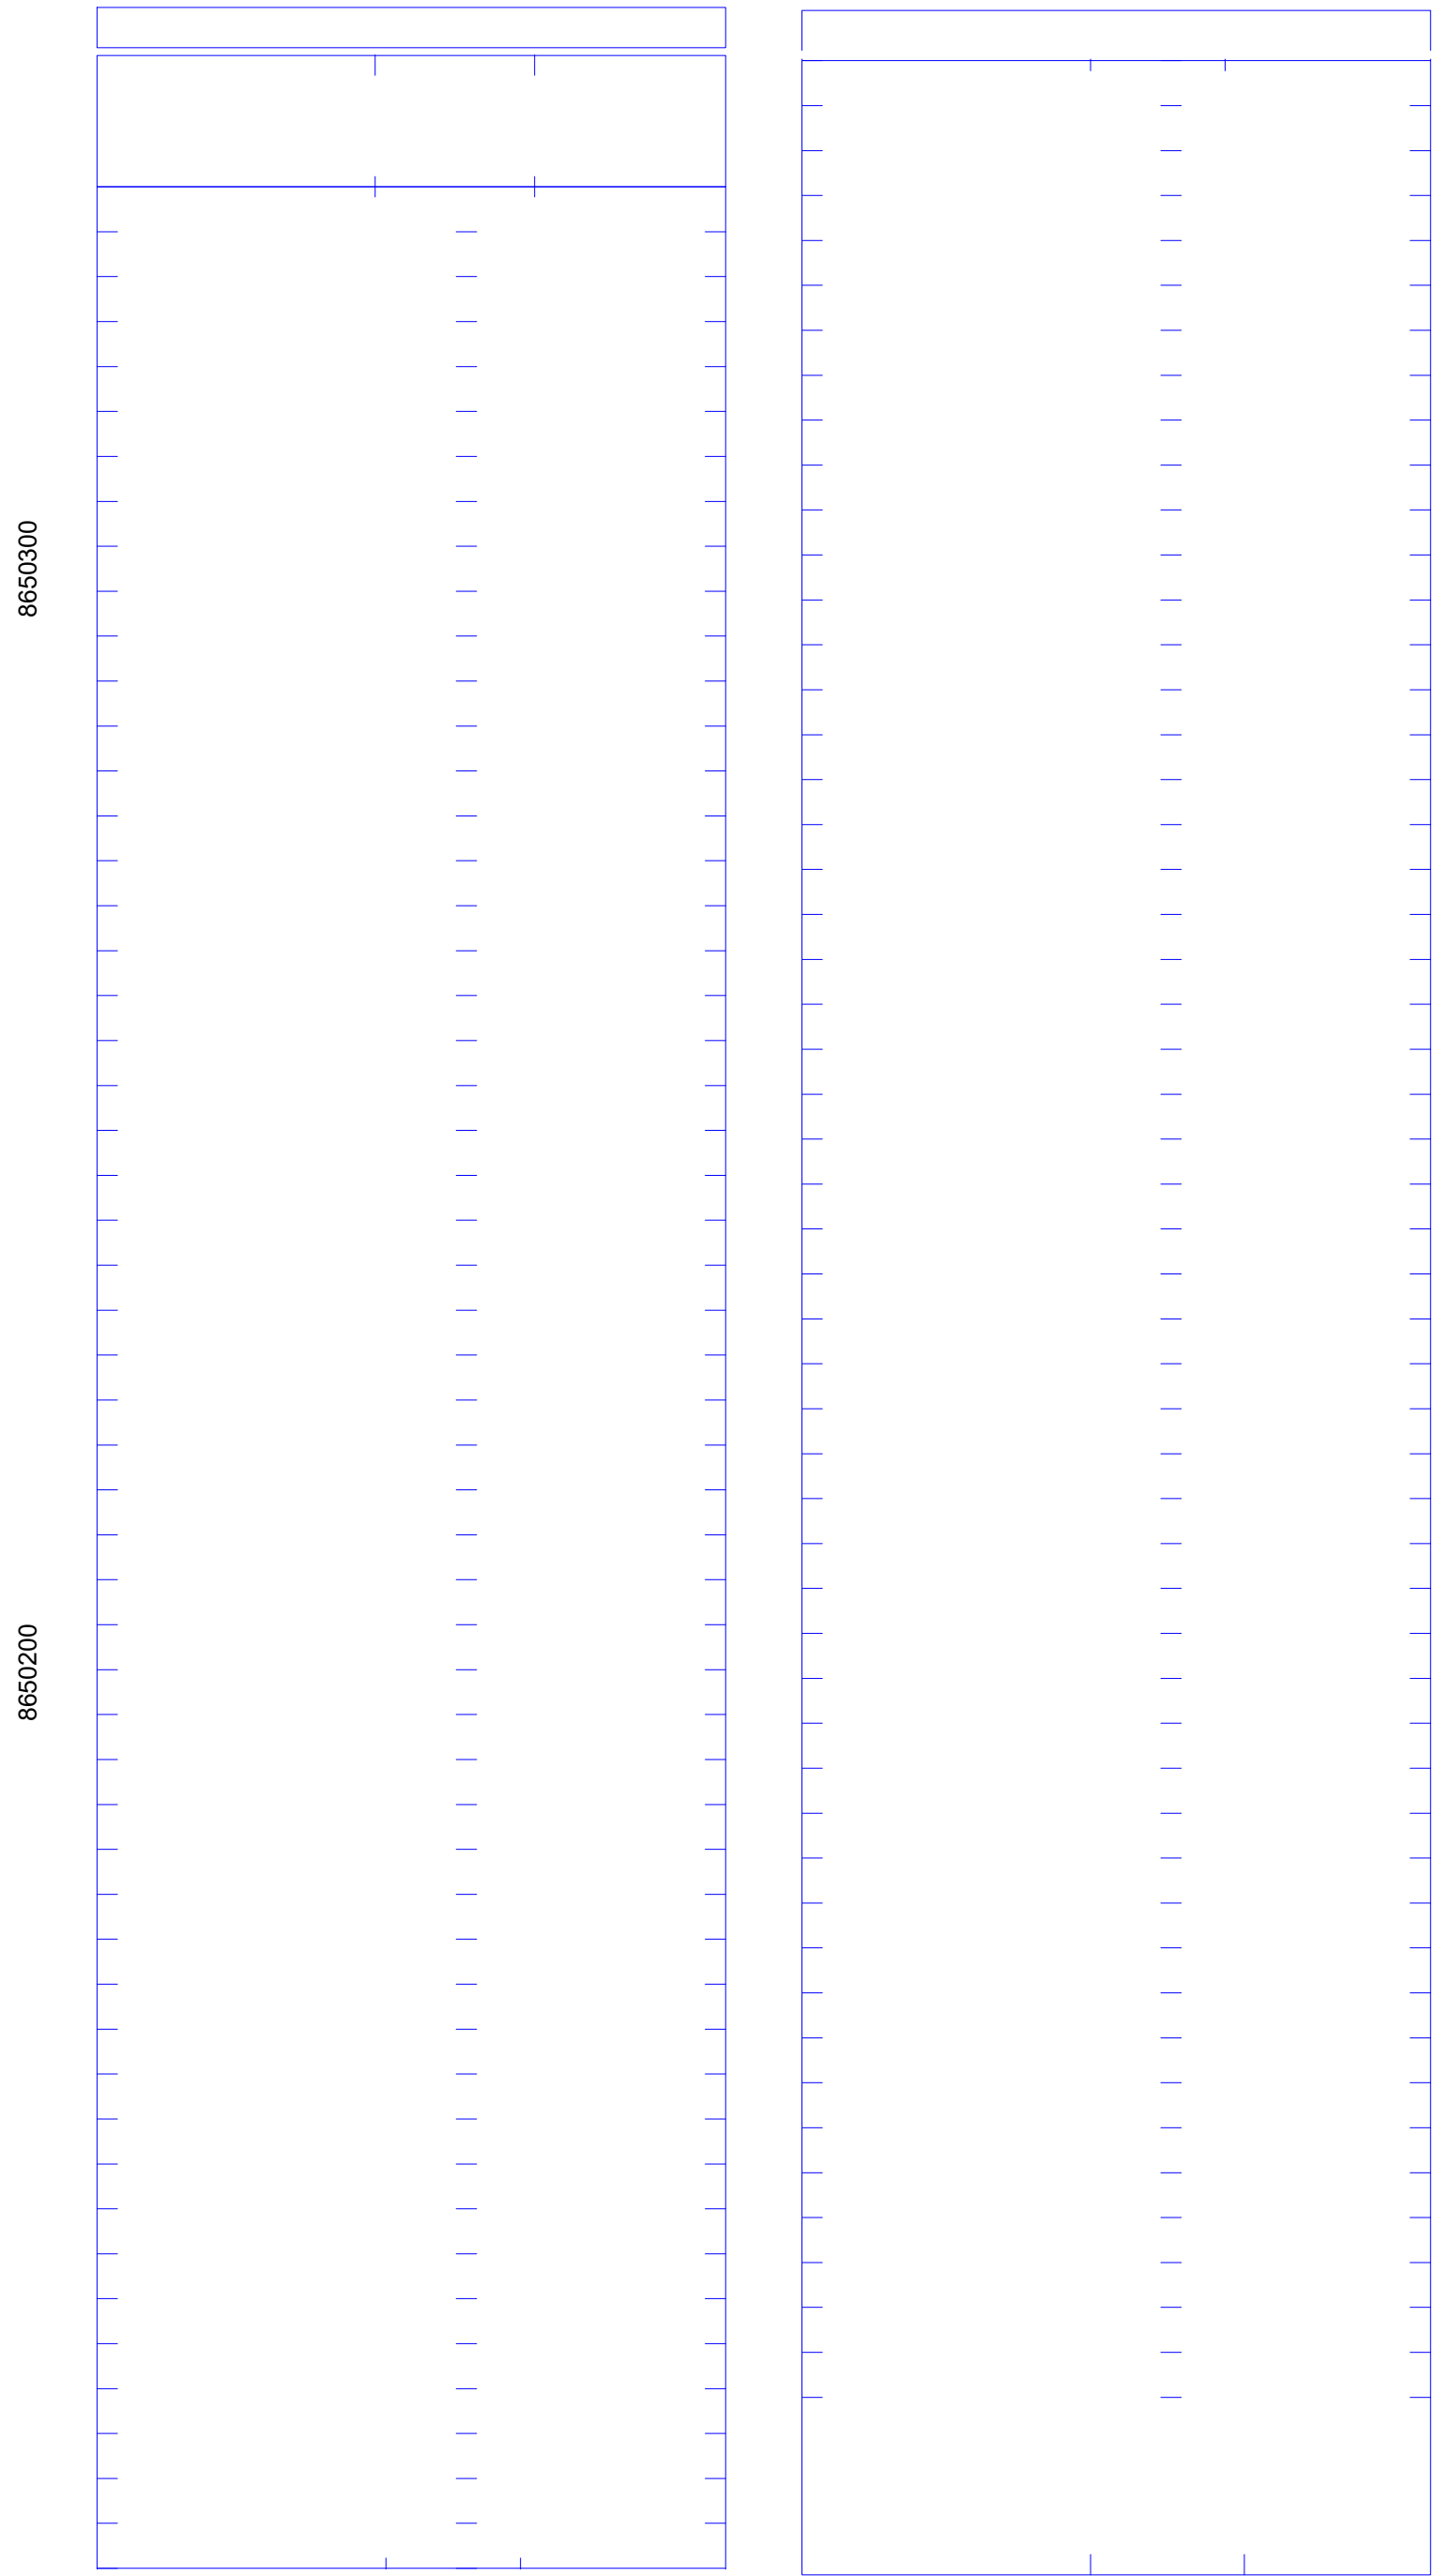


8650300

002058

8650100

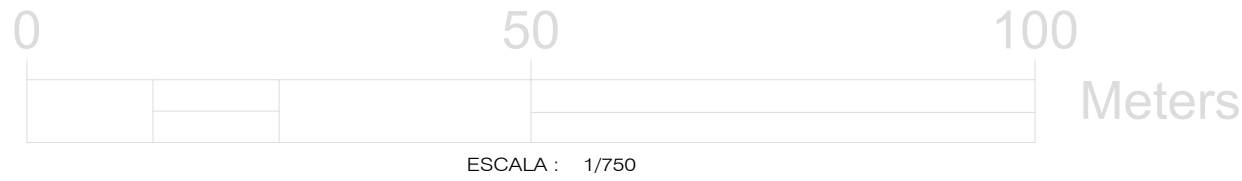

ESCALA : 1/750

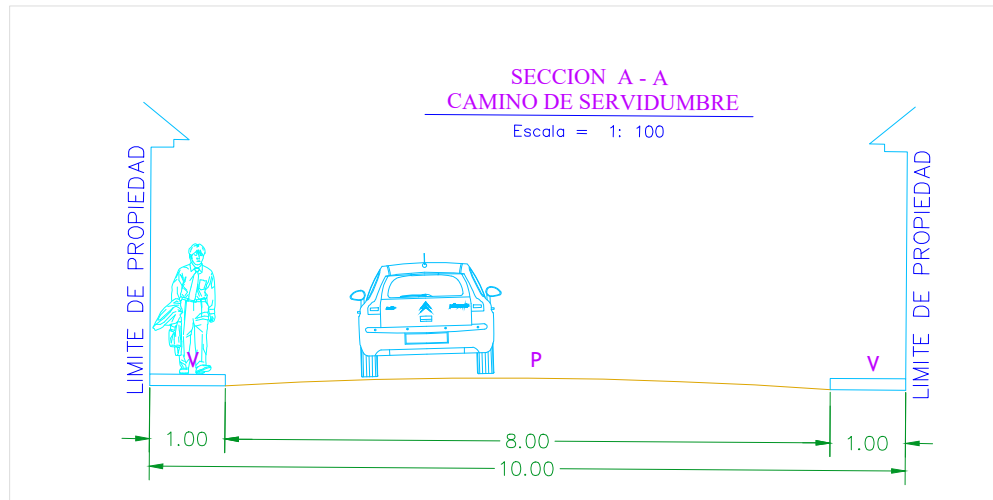

PROPIETARIO : PANORAMA S.A.C.		PROFESIONAL :	
PLANO : INDEPENDIZACION		DATUM : WGS 84 ZONA : 18 SUR	
UBICACION : Partida Electronica N° 12887154 PRECIO : PARCELA ADRIAN LEON REYES 1 SECTOR : EL MANZANO PAMPA EL TARO DISTRITO : SANTO DOMINGO DE LOS OLIVEROS PROVINCIA : HUARACHIRI DEPARTAMENTO : LIMA		LAMINA : I-01 Area = 103,854.6122 m2 Perimetro = 1380.037 ml	
FECHA : LIMA, enero - 2023		ESCALA : 1/750	